


สำเนา

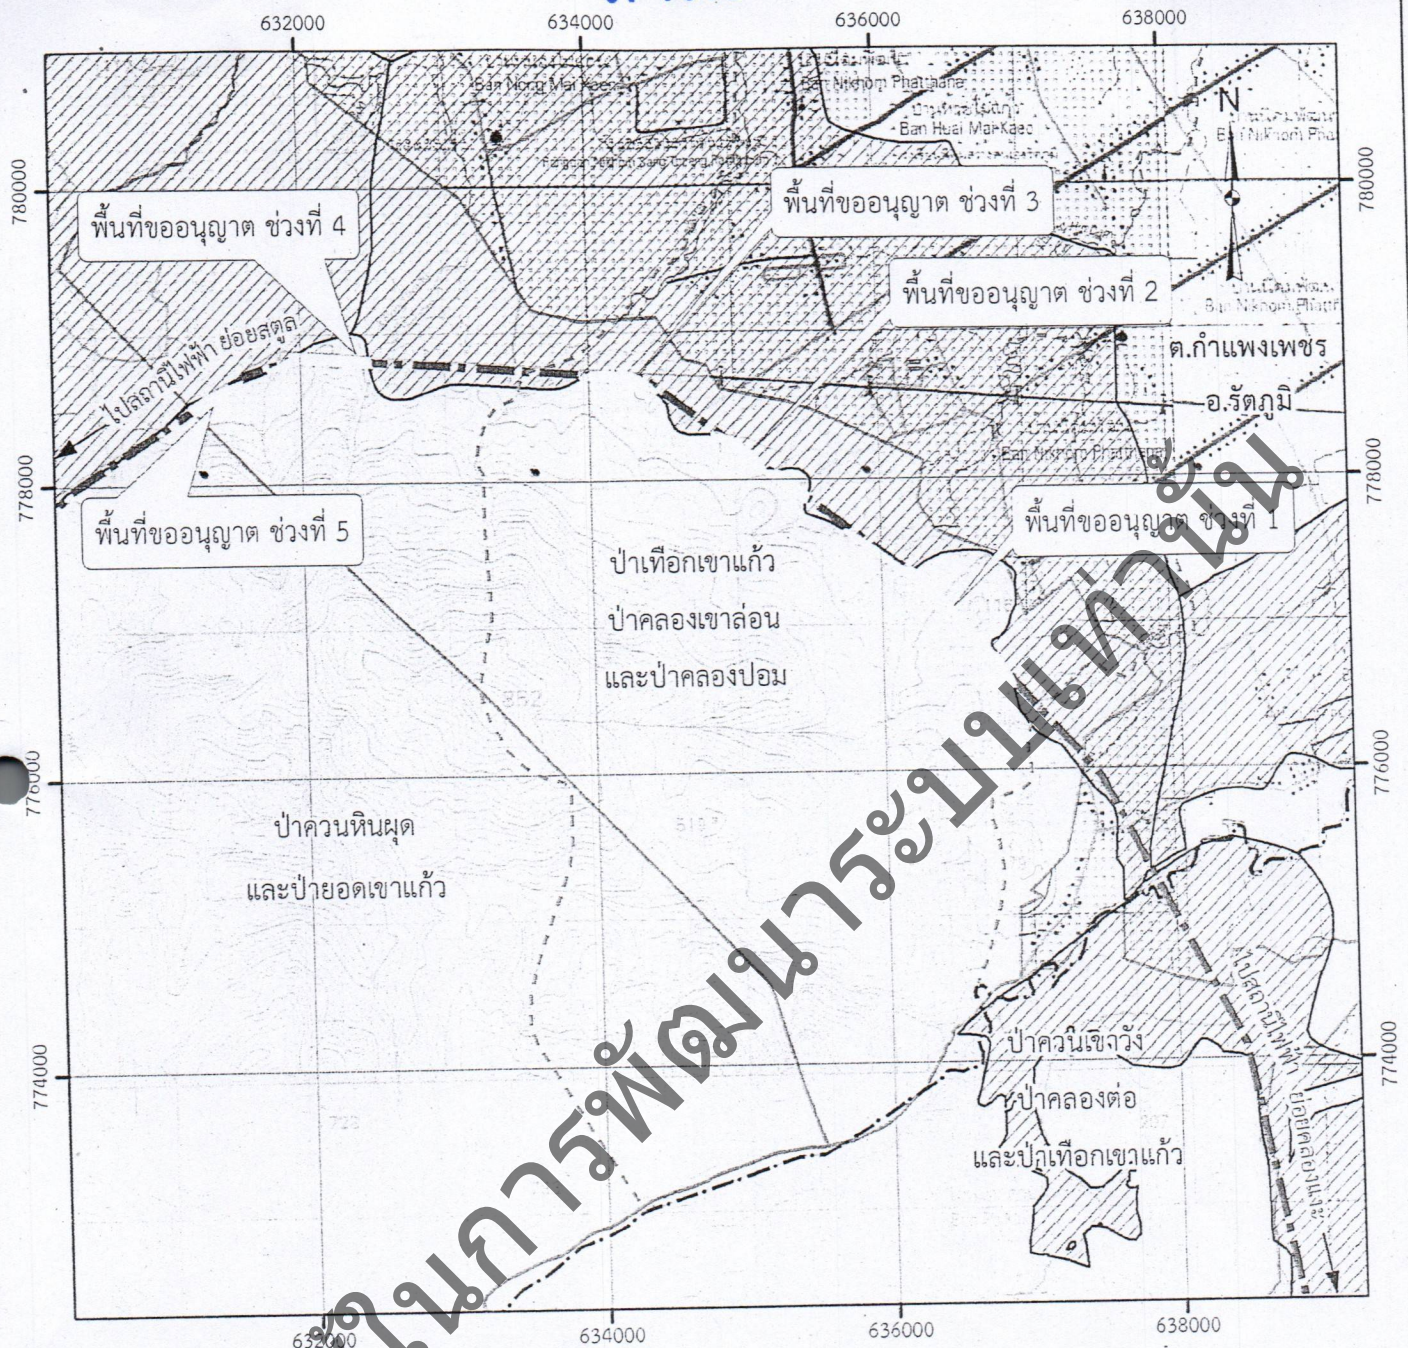


คำอธิบายสัญลักษณ์

-  ระบบโครงข่ายไฟฟ้า 230 กิโลโวลต์ คลองแฉะ - สตูล (ช่วงที่ 1) (ช่วงปรับแก้ทิศทางและแนวเขตระบบโครงข่ายไฟฟ้า) มีขนาดความกว้างจากแนวศูนย์กลางของเสาสายส่งไฟฟ้าด้านละ 25 เมตร (รวมทั้งสองด้านกว้าง 50 เมตร)
-  พื้นที่ขออนุญาตเข้าทำประโยชน์ภายในเขตป่าสงวนแห่งชาติป่าเทือกเขาแก้ว ป่าคลองเขาล่อน และป่าคลองปอม เนื้อที่ 94-2-56 ไร่

--- แนวเขตอำเภอ

--- แนวเขตตำบล

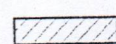 พื้นที่เขตปฏิรูปที่ดิน

 พื้นที่เขตป่าสงวนแห่งชาติ

สำเนาถูกต้อง

0 0.250.5 1 1.5 2 กิโลเมตร

(นายรัช ทองอิม) มาตรฐาน 1 : 50,000

เจ้าพนักงานป่าไม้ชำนาญงาน L7018 กรมแผนที่ทหาร

พื้นหลักฐาน WGS 84 UTM ZONE 47N ระหว่าง 5022 IV, 5023 III

การไฟฟ้าฝ่ายผลิตแห่งประเทศไทย

แผนกขอใช้ที่ดิน กองจัดหาที่ดิน ฝ่ายที่ดิน

แผนที่ภูมิประเทศมาตราส่วน 1:50,000 แสดงบริเวณพื้นที่ที่ กฟผ. ขออนุญาต เข้าทำประโยชน์ภายในเขตป่าสงวนแห่งชาติ เพื่อก่อสร้างและบำรุงรักษาระบบ โครงข่ายไฟฟ้า 230 กิโลโวลต์ คลองแฉะ - สตูล (ช่วงที่ 1) (ช่วงปรับแก้ทิศทางและ แนวเขตระบบโครงข่ายไฟฟ้า) ท้องที่ ต.ท่าชะมวง ต.เขาพระ อ.รัตภูมิ จ.สงขลา

เขียน นายไกรสร น้อยพุก

วันที่ 19/07/2566

ตรวจ นายธีระวุฒิ เกิดศิริ

แบบเลขที่ 1-KNE-STU-21/07/23.077